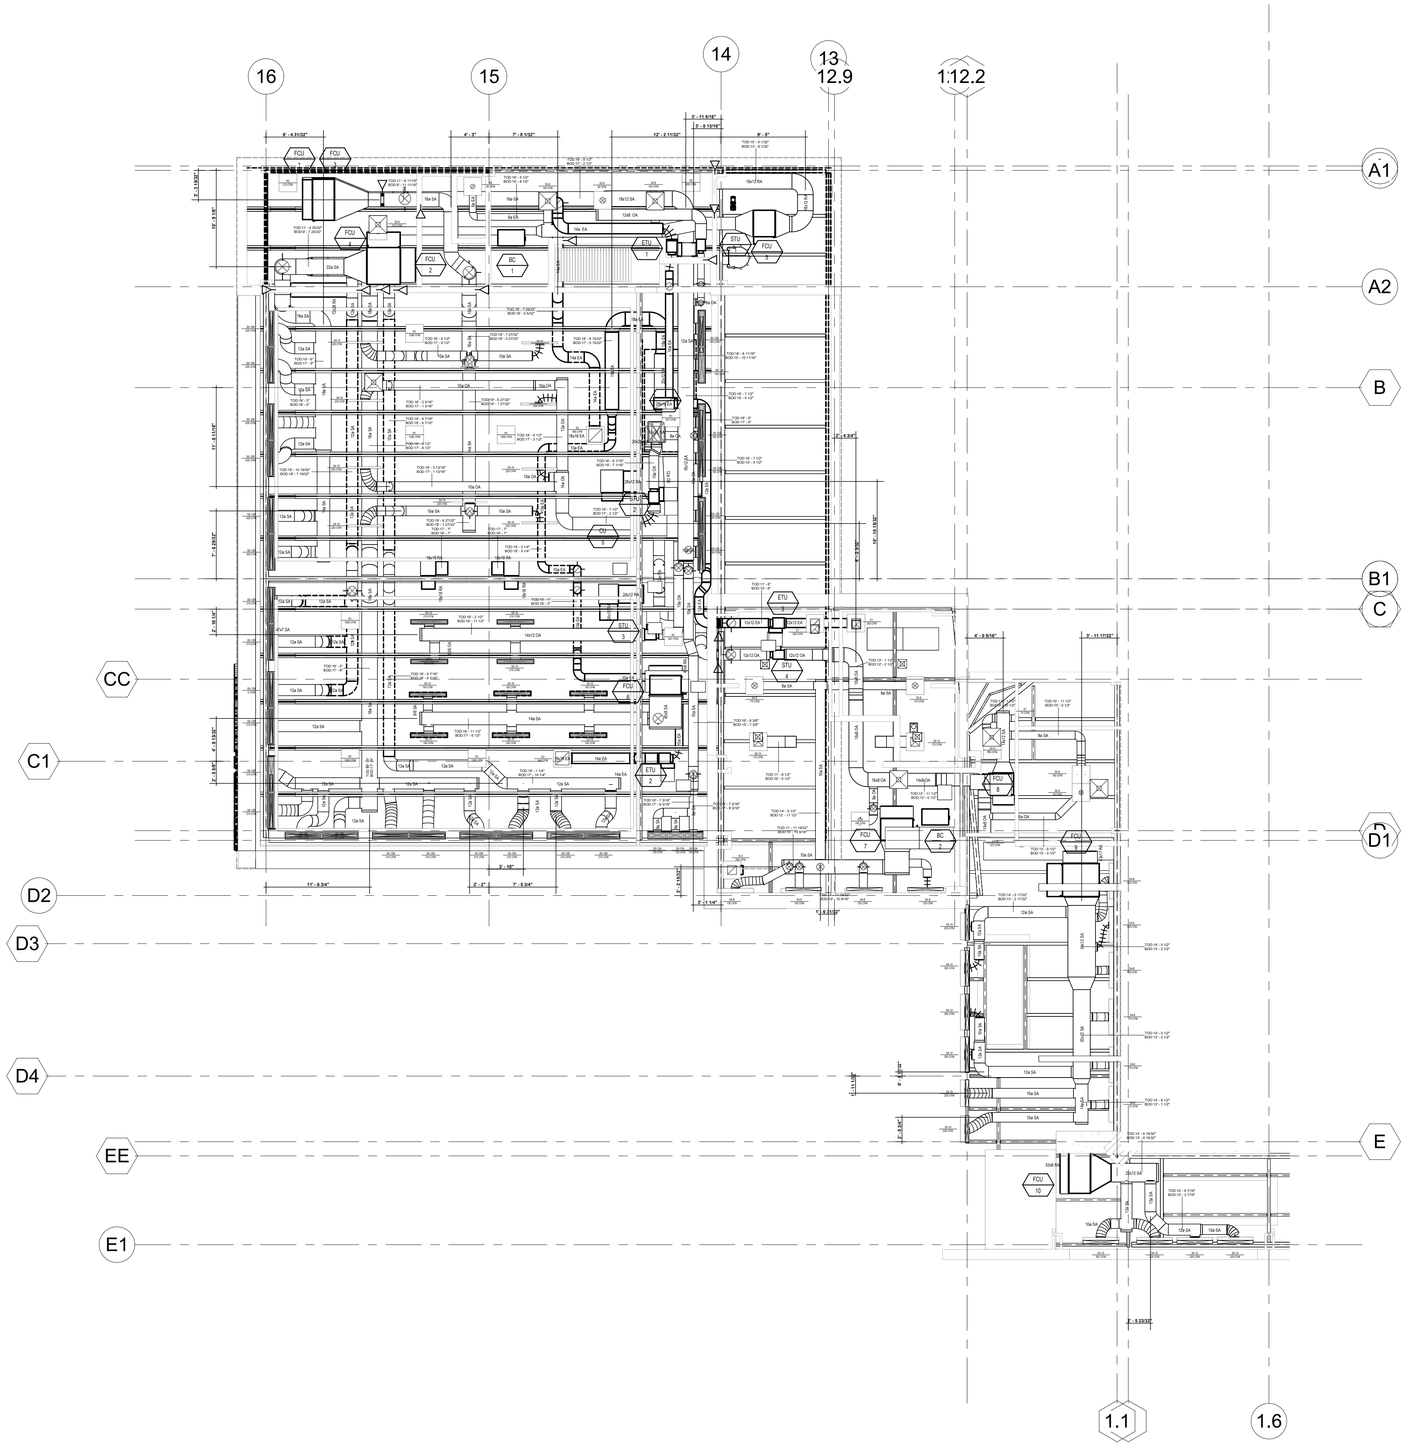

1 RJO shop drawing
1/8" = 1'-0"

R.J. OLMEN COMPANY
VENTILATION CONTRACTORS
SINCE 1972
(847) 724-0994 RJOLMENCOMPANY.COM

PUBLIC BUILDING COMMISSION

CITY COLLEGES of CHICAGO

WSLC ADDITION & RENOVATIONS

4624 WEST MADISON ST.
CHICAGO IL 60644

CITY COLLEGES OF CHICAGO

CITY OF CHICAGO, MAYOR BRANDON JOHNSON

Architect of Record:
bailey edward

ADDRESS: 35 EAST WACKER DR
SUITE 800
CHICAGO, IL. 60601-2308
PHONE: 312.440.2300
FAX: 312.440.2303
WEB: www.baileyedward.com

©2024 Bailey Edward Design

Design Firm License No. 184-001962

RME
200 S. Michigan Ave. Suite 1500
Chicago, IL. 60604
312.870.6638
Structural Engineers of Record &
Civil Engineers of Record

Hitchcock Design Group
22 E. Chicago Ave.Suite 200
Chicago, IL 60540
630-961-1787
Landscape Architects of Record

Environmental Design International inc.
33 West Monroe Street Suite 1825
Chicago, IL 60603
312-345-1400
Environmental Reno/Demo & Surveyor

RTM
250 S. Wacker Dr. Suite 400
Chicago, IL 60606
312-216-0507
MEPFP Engineers of Record

HUS Architecture
2202 S. Halsted Street.
Chicago, IL 60608
312-224-8048
LEED Consultant

Issuance

Mark	Description	Date
	95% CD	12/07/2023
KSB	Coordinated Shop Drawing	8/15/2025

PBC Project Name:
West Side Learning Center
Addition and Renovations

PBC Contract No: PS3036

Project No.: BED 022137 / PBC 03720

Title
DUCTWORK SHOP DRAWING

Sheet
M-02

C:\Users\kevin.000\OneDrive - R.J. Olmen Company\RJO BIM FOLDER\MXC-RJO-BIM\MXC_RJO_Ventilation.rvt
8/15/2025 3:12:43 PM