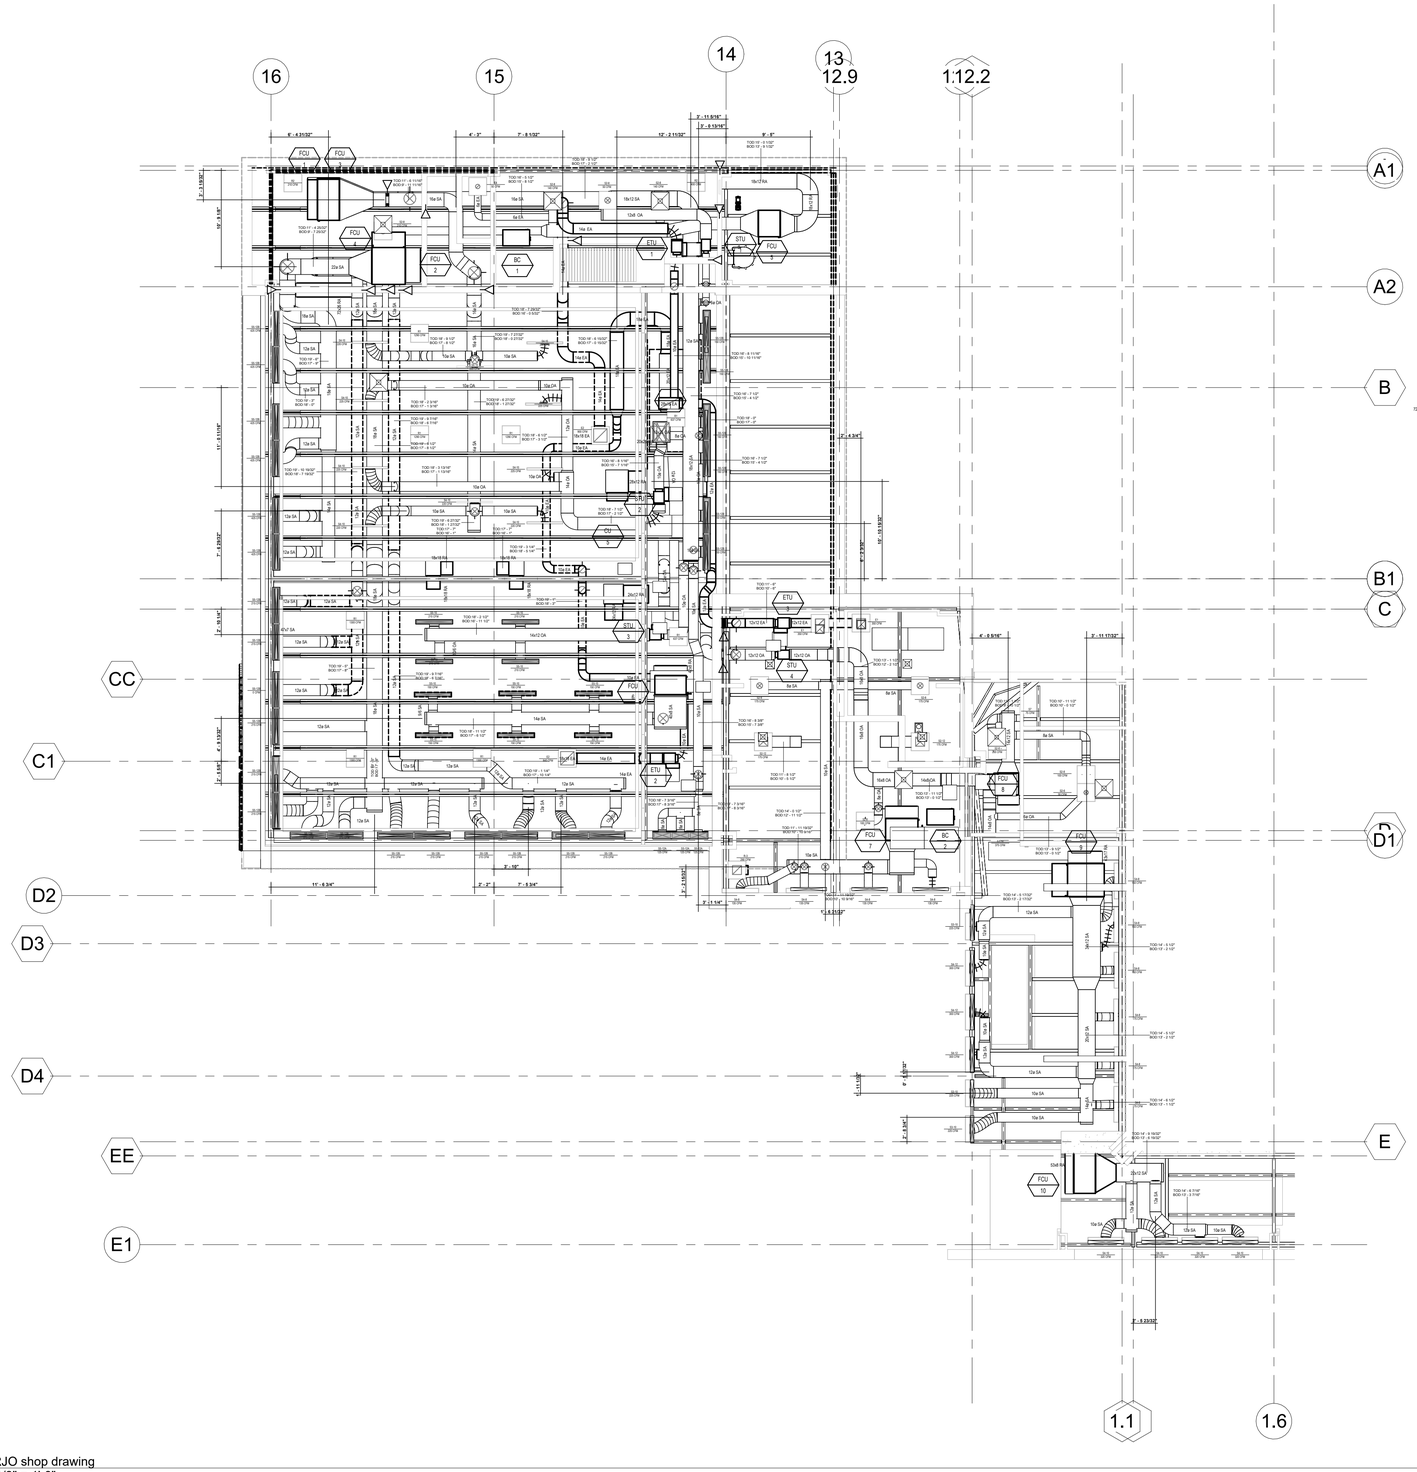

1 RJO shop drawing
1/8" = 1'-0"

R.J. OLMEN COMPANY
VENTILATION CONTRACTORS
SINCE 1972
(847) 724-0994 RJOLMENCOMPANY.COM

[redacted]

Issuance

Mark	Description	Date
	95% CD	12/07/2023
KSB	Coordinated Shop Drawing	8/15/2025

[redacted]

DUCTWORK SHOP DRAWING

Sheet M-02

C:\Users\kevin.000\OneDrive - R.J. Olmen Company\RJO BIM FOLDER\MXC-RJO-BIM\MXC_RJO_Ventilation.rvt
8/15/2025 3:12:43 PM